ENTRÉE PRINCIPALE

Pas de stockage des PF
Une navette journalière la fin de la journée (au minimum) pour la livraison des produits semi - finis Vers l'usine voisine de la même propriétaire pour la métallisation

Le bloc administratif est classé type W .
Conformément aux dispositions particulières du type W, une dérogation à l'article CO 52 §3 est applicable :
**Bâtiment en R+2 (3 niveaux, dont RDC)*
**Aucun local à risques particuliers en communication directe avec les volumes accessibles au public*
→ L'encloisonnement des escaliers n'est donc pas requis.

Non Conformité de l'article 26
Objet d'une demande de dérogation
(Voir notice page la page 7)

Mur H=2.2m

(EXTRACTION MÉCANIQUE)
02 VENTILATEURS HÉLICOÏDALE ASSERVIES À LA DÉTECTION INCENDIE REQUISES PAR UNE COMMANDE MANUELLE
(Voir detail)
AVEC UN DÉBIT UNITAIRE D'EXTRACTION = 7 500 m3/H

Séparation en plaque de plâtre CF2H jusqu'à la toiture

VOLET À LAMELLES 600*600

VENTILATEUR AXIAL DEBIT=7500 m3/h–400°C/2h

Plateforme de déchargement des matériaux
S = 99.7 m²
H = 8.80m
H' = 7.30m
Hréf = 8.05m
05 Personnes
(Faux plafond en plâtre)

Dépôt matières Brutes
S = 346.2 m²
H = 8.80m
H' = 7.30m
Hréf = 8.05m
(Couverture en Charpente métallique)

Salle de décassage et de mélange
S = 62.7m²
HSP = 6.00m
04 Personnes
(Faux-plafond en plaque de plâtre)

Atelier d'usinage
S = 82m²
HSP = 6.00m
05 Personnes
(Faux-plafond en plaque de plâtre)

Tour CNC 2KW | Fraiseuse 3KW | Rectifieuse 1.5KW | Découpage au laser 7KW

Séparation grillagée H=2.00m

Façade NORD-OUEST
Mur H=2.2m

Dépôt matières bruts
S totale = 346.2m² > 300m²

Désenfumage de cette salle sera réalisé en **Naturel/Mécanique**
Surface d'amenées d'air
Les amenées d'air sont assurées par :
- 01 porte à la française de 1.00m × 2.50m
La surface des amenées d'air frais est :
1mx2.5m = 2.5 m² > 0.5% de la surface = 1.73 m²

Débit d'extraction des fumées
$Q_{extraction}$ = 1m3/s/100m² + 20% (débit de fuite tolérable)
$Q_{extraction}$ =346.2m²/100m²× 3600 × 1.2 = 14955.84 m³/h
L'évacuation des fumées sera assurée par 02 Ventilateurs Hélicoïdales d'extraction de désenfumage agrée F400-120 (400°C-2H) selon la norme NF en 121 01-3, et asservie à la détection automatique d'incendie de débit unitaire de 7 500m³/H, totalisant 15 000 m3/H.

Bâche à eau enterrée V=91m³

Façade SUD-EST
Mur Bahût H=0.9m

ENTRÉE SECONDAIRE PIETONNE (NON VEHICULAIRE)

Voie 1

Entrée Administration

Entrée ouvrier

Bureau S = 9m² H 4.00m 01 Personnes

Hall d'accueil S = 37.8 m² H = 3.20m 02 Personnes (Couverture en dur)

SAS Accès Visiteur S = 7.4 m²

Zone d'exposition S = 25.2 m²

Salle d'inspection de la qualité 2 S=42.5m² H=3.20m 05 Personnes

Hall S=14m²

SAS Accès Employés S = 8.6 m²

Salle d'inspection de la qualité 1 S=15m² H=3.20m 04 Personnes

SAS S=4.6m²

L. Surpresseur S=7m²

Local réservoir chantier Non accessible

Non exploitable S=9m² H=3.00m (Couverture en dur)

Poste Transfo. S=9m² H=3.10m (Couverture en dur)

02 Pompes de 10m³/H - 85m pour l'alimentation des RIA dont 01
Pomme de secours
Bassin de capacité de 500 litres

VERS ETAGES

Salle 2 pour additionner les matériaux S=138.1m² HSP = 3.00m (Faux-plafond en plaque de plâtre)

Salle 3 pour additionner les matériaux S=129.1m² HSP = 3.00m (Faux-plafond en plaque de plâtre)

Grille de800x200 avec Dumper

Séparation en panneau de purification

Atelier d'injection Plastique
Capacité de production Journalière < à 1t/jrs
S = 892.2 m²
HSP = 6.00
16 Personnes
(Faux-plafond en plaque de plâtre)

Séparation en panneau de purification

Tables d'ajusteur

Stockage du support de moule S = 43.2m² HSP = 6.00m (Faux-plafond en plaque de plâtre)

VERS MEZZANINE

Salle de montage des manipulateurs S=37.2m² H = 3.10m 05 Personnes (Couverture en Dur)

Bloc Sanitaire S = 13.8 m²

Zone Technique (Compresseur) S = 43.7m² H = 4.00m (Sous abri)

Refroidisseur d'air 1 P = 67 KW

Refroidisseur d'air 2 P = 67 KW

Ecrasement d'air P = 55 KW

Plateforme en structure d'acier 3m

Escalier desservant une mezzanine => Pas d'enclosonnement

VENTILATEUR AXIAL d'extraction DEBIT=21000 m3/h–400°C/2h à 35 mmCE

A prévoir pour l'Evacuation des fumées :
Gaine montante en terrasse de 600mm×500mm pour le désenfumage vers tourelle d'extraction résistant au feu 400°C/2H et asservie à la détection automatique incendie
Débit d'extraction = 21000 m³/h

Volet 800/550 en terrasse

Zone extracteurs des fumées des machines S = 42m²

VENTILATEUR AXIAL DEBIT=13000 m3/h–400°C/2h

VOLET À LAMELLES 600*600

(EXTRACTION MÉCANIQUE)
03 VENTILATEURS HÉLICOÏDALE ASSERVIES À LA DÉTECTION INCENDIE REQUISES PAR UNE COMMANDE MANUELLE
(Voir detail)
AVEC UN DÉBIT UNITAIRE D'EXTRACTION = 15 000 m3/H

Façade NORD-EST
Mur H=2.2m

PLAN RDC
ECH : 1/100

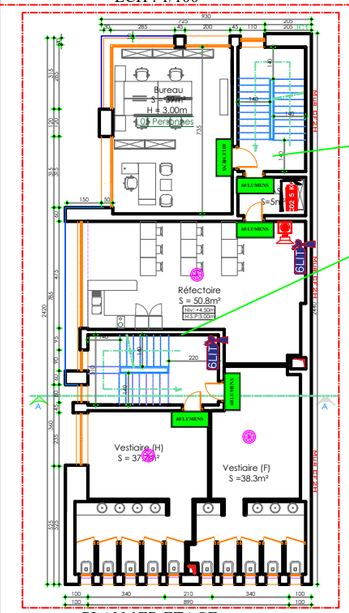

PLAN 1ER ETAGE
ECH : 1/100

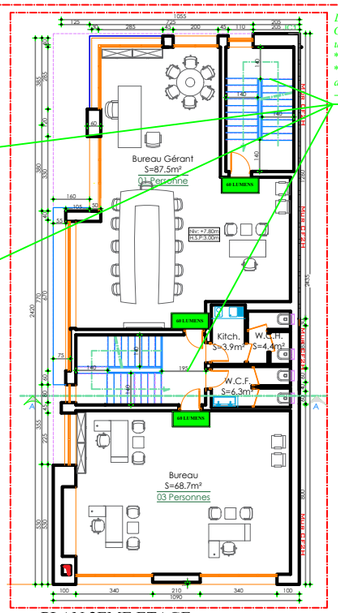

PLAN 2EME ETAGE
ECH : 1/100

Le bloc administratif est classé type W .
Conformément aux dispositions particulières du type W, une dérogation à l'article CO 52 §3 est applicable :
**Bâtiment en R+2 (3 niveaux, dont RDC)*
**Aucun local à risques particuliers en communication directe avec les volumes accessibles au public*
→ L'encloisonnement des escaliers n'est donc pas requis.

Escalier desservant une mezzanine => Pas d'enclosonnement

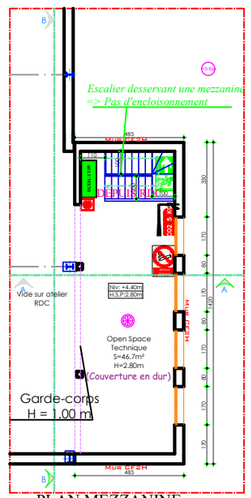

PLAN MEZZANINE
ECH : 1/100

Les 04 salles (Atelier d'injection Plastique + Deux zones pour additionner les matériaux et Stockage du support de moule sont séparées par des cloisons légères, non coupe-feu.
En cas d'incendie, la propagation des fumées est rapide.
Un désenfumage commun est donc justifié.

S_{totale} = 1344.8m² > 300m²
L = 59.90m

Le désenfumage de cette salle sera réalisé en **Naturel/Mécanique**
Surface d'amenées d'air
Les amenées d'air sont assurées par :
- 01 porte rideaux de 2.50m × 3.50m
- 02 portes à la française de 1.00m × 2.50m
La surface des amenées d'air frais est :
[(2.5mx3.5m)+(2×(1mx2.5m))]
= 13.75 m² > 1% de la surface = 13.44 m²

Débit d'extraction des fumées
$Q_{extraction}$ = 1m3/s/100m² + 20% (débit de fuite tolérable)
$Q_{extraction}$ =1344.8m²/100m²× 3600 × 1.2 = 58 095.36 m³/h
L'évacuation des fumées sera assurée par 03 Ventilateurs Hélicoïdales d'extraction de désenfumage agrée F400-120 (400°C-2H) selon la norme NF en 121 01-3, et asservie à la détection automatique d'incendie de débit unitaire de 13 000m³/H, et par 01 Tourelles d'extraction de désenfumage agrée F400-120 (400°C-2H) selon la norme NF en 121 01-3, et asservie à la détection automatique d'incendie de débit de 21 000m³/H, dont il seront muni d'un réseau de gaine rectangulaire et des grilles d'extraction.
Les ventilateurs et les tourelles totalisant 60 000 m3/H

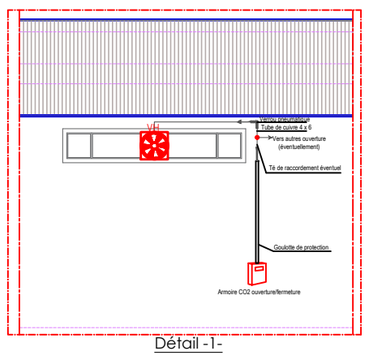

Détail -1-
Commande Ouverture / Fermeture
Désenfumage mécanique par Ventilateur hélicoidale en façade

LÉGENDE D'ÉVACUATION

	Bloc autonome de 60 Lumens avec indication "Sortie de secours"
	"Flèche" d'indication de sens d'évacuation
	Point de rassemblement personnels et visiteurs
	Cheminement d'évacuation

LÉGENDE DES MOYENS D'INTERVENTION

	Robinet d'Incendie Armé DN33
2Kg	Extincteur à CO2 de 5Kg
6LITRES	Extincteur à eau pulvérisé de 6Litres
6KGS	Extincteur à poudre ABC de 6Kg
	Boite Pharmacie

LÉGENDE DE DÉTECTION AUTOMATIQUE INCENDIE

	Détecteur optique de fumée
	Détecteur thermo-vélocimétrique
	Détecteur de fuite de Gaz
	Détecteur Linéaire de fumée (Emetteur / Récepteur + Réflecteur)
	Sirène d'alarme
	Bouton bris de glace
CDI	Centrale de Détection Incendie
T.RE	Tableau de Report

LÉGENDE CONSIGNES DE SÉCURITÉ

CGS	Consignes générales de sécurité
CSg	Consigne spéciale pour le gardien
CSei	Consigne spéciale pour l'équipe d'incendie
CSPT	Consigne de sécurité particulières du poste transformateur
CPSST	Consigne particulières de santé et sécurité sur le poste de travail

LÉGENDE D'AFFICHAGE ET SIGNALISATION

	Défense de fumer
	Défense d'entrer
	Numéros d'urgences

LÉGENDE DE DESENFUMAGE

VB	Ventilation Basse Naturel
VH	Ventilation Haute Mécanique (V. Hélicoidale)
	Déclenchement manuel de désenfumage mécanique

NORD

REPUBLIQUE TUNISIENNE
GOUVERNORAT DE MONASTIR
COMMUNE DE SAHLINE

USINE D'INJECTION PLASTIQUE
(FABRICATION DES DIVERS ARTICLES EN MATIÈRE PLASTIQUE : BOUCHON, COFFRET ET BOÎTIER DE MAQUILLAGE...)
"STÉ MYD TUNISIA"
LOT 110 S - ZONE INDUSTRIELLE NEOPARK DE MONASTIR
ROUTE DE SAHLINE - 5012

GÉRANT :
MR. SAMI LADJIMI

PLAN N° : 3/3

DATE :
COPIE 1 - OCTOBRE 2025

ECHELLE: 1/100

*PLAN D'ENSEMBLE DE RDC - MEZZANINE & 2 ÉTAGES D'IMPLANTATION DES MOYENS D'INTERVENTION ET DE LUTTE CONTRE L'INCENDIE, D'AFFICHAGE, D'INSTALLATION D'ALARME ET DE DETECTION AUTOMATIQUE D'INCENDIE, DU DESENFUMAGE ET D'EVACUATION

BUREAU D'ÉTUDE
Nom : Polycompétence Consulting
Siège social : Immeuble Ennasr, Avenue du Combattant Suprême 5000 MONASTIR
Tél. / Fax: (+216) 73 425 430
E-mail : saber.bs@planet.tn

DESSINÉ PAR :
SOUROUR AJEJ

POLYCOMPÉTENCE CONSULTING